


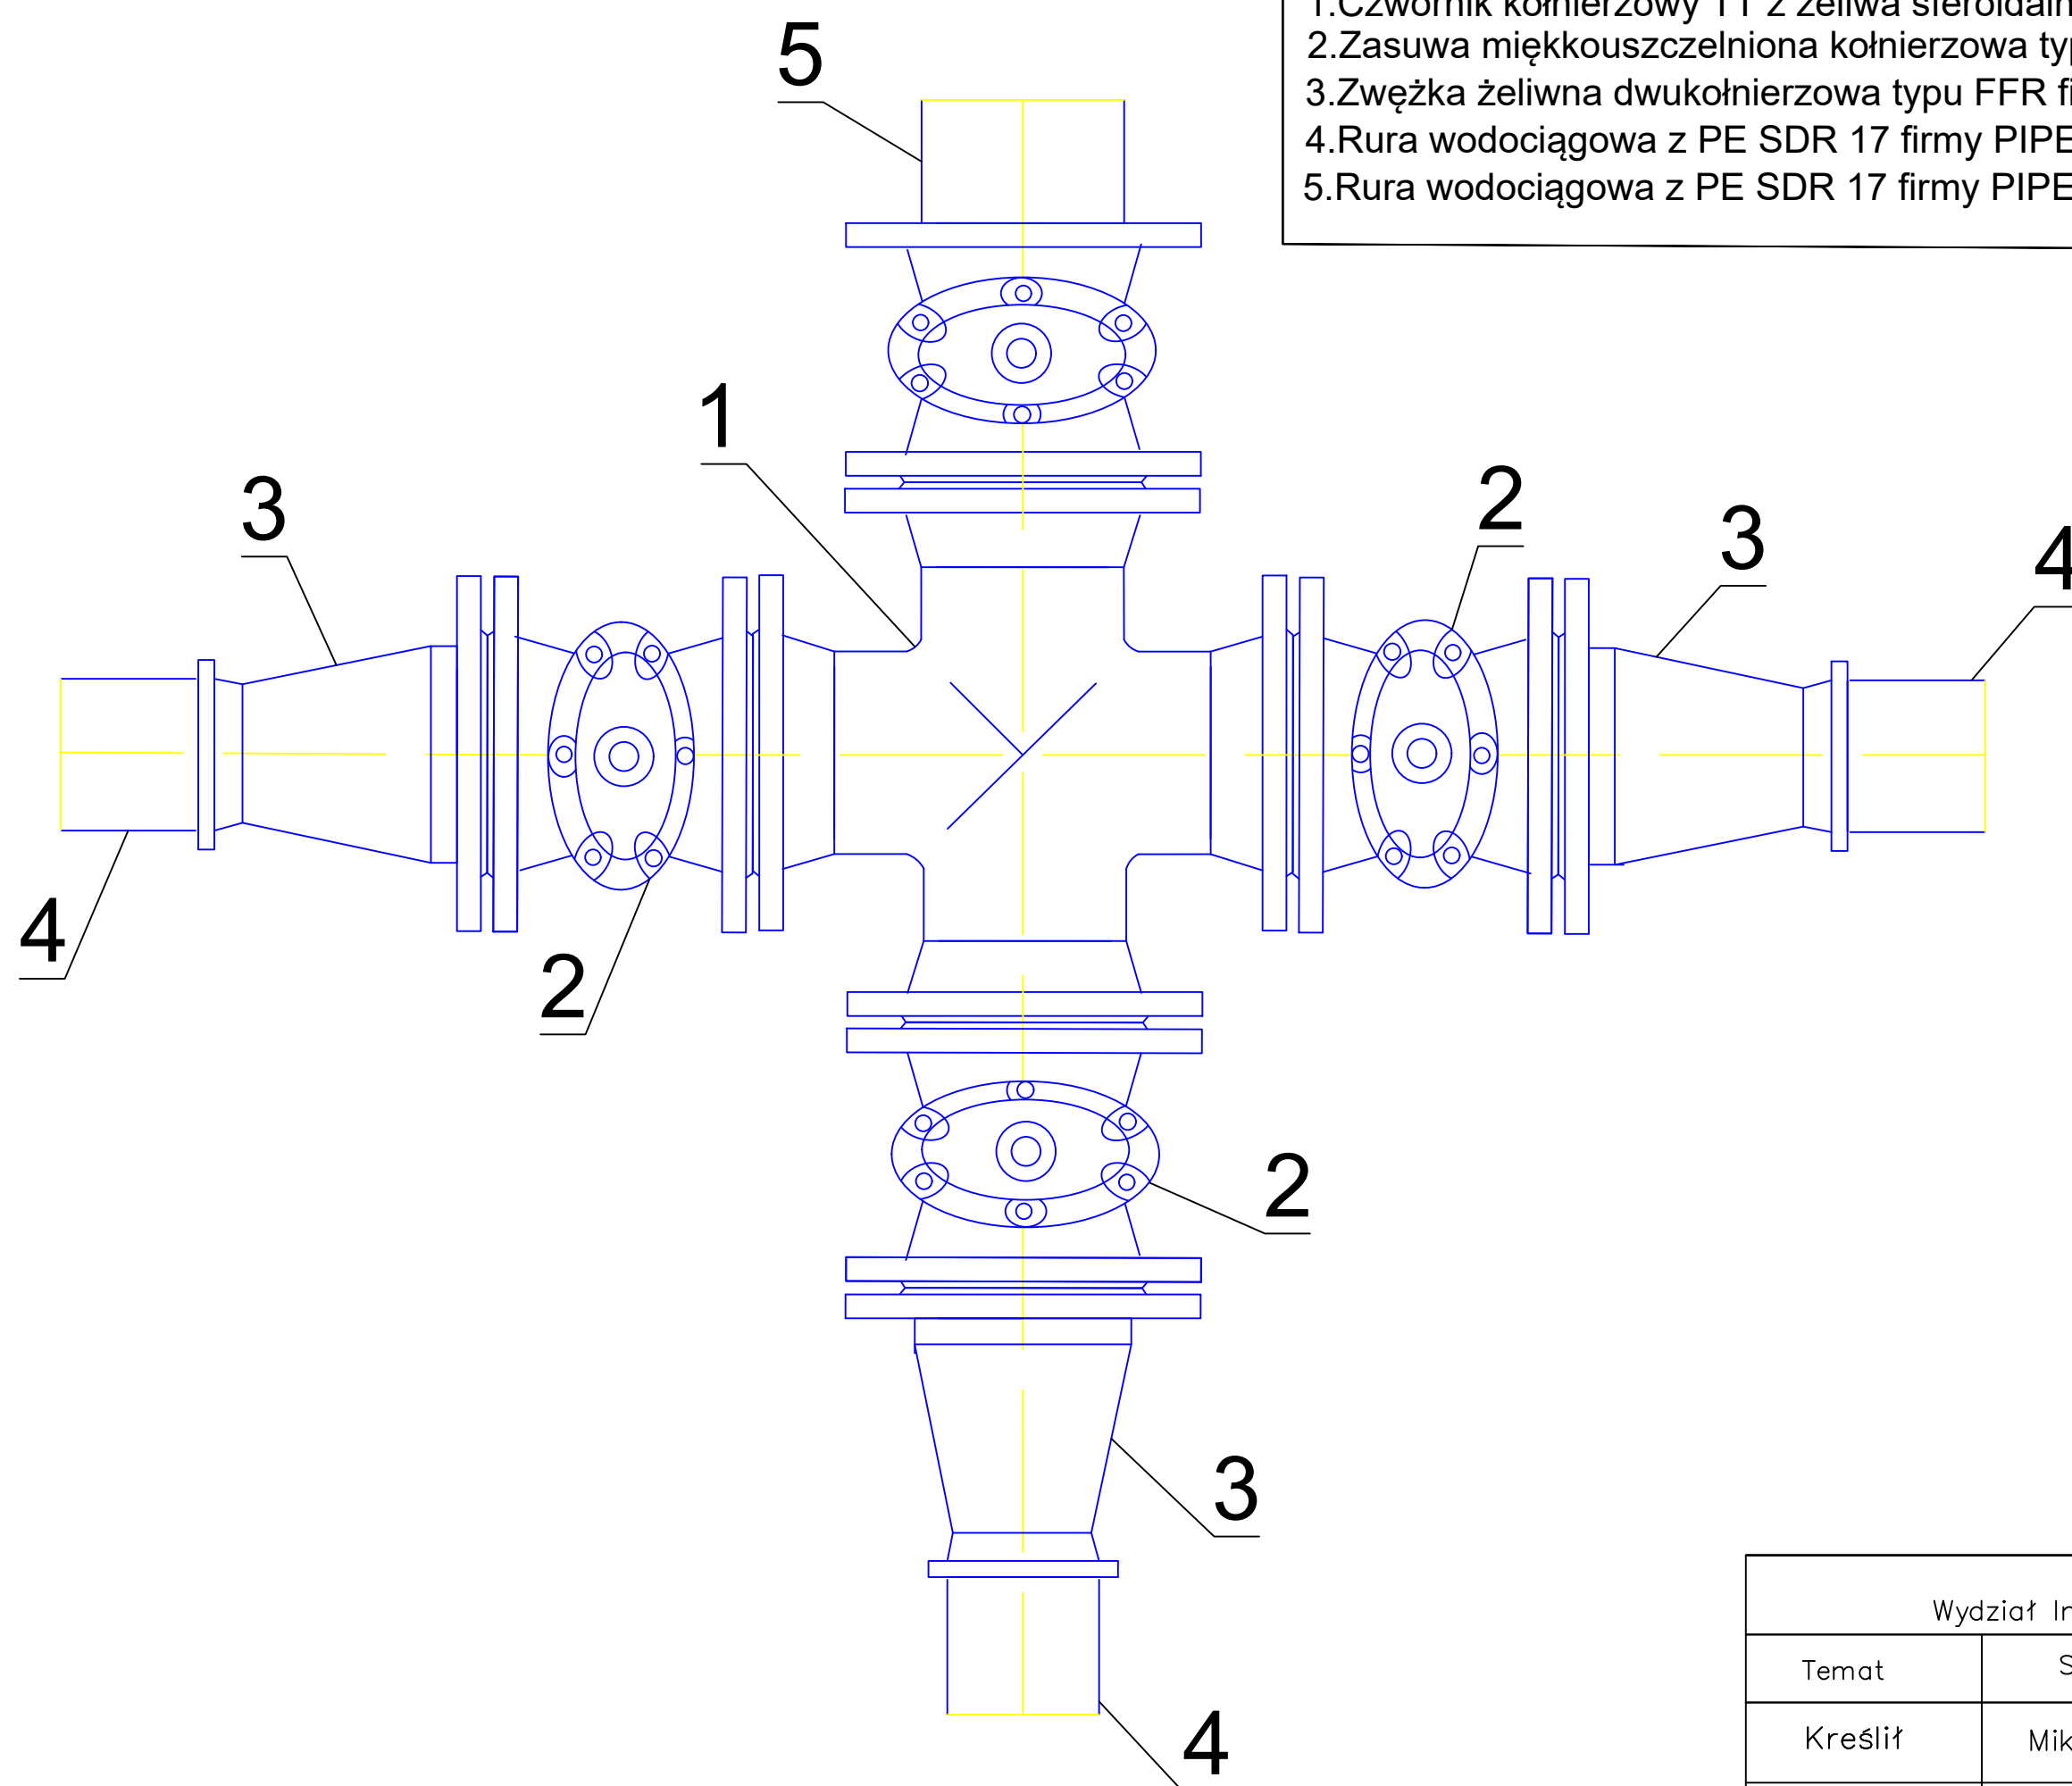

- Zestawienie podstawowych materiałów:
- 1.Czwórnik kołnierzowy TT z żeliwa sferoidalnego DN 300
 - 2.Zasuwa miękouszczelniona kołnierzowa typu 2002-2111 firmy Jafar (4 sztuki)
 - 3.Zwężka żeliwna dwukołnierzowa typu FFR firmy Jafar
 - 4.Rura wodociągowa z PE SDR 17 firmy PIPELIFE DN 225 (3 sztuki)
 - 5.Rura wodociągowa z PE SDR 17 firmy PIPELIFE DN 280

Politechnika Lubelska			
Wydział Inżynierii Środowiska i Energetyki			
Temat	Schemat węzła	Skala:	1:10
Kreślił	Mikta Rymasheuski	Numer:	7
Sprawdziła	dr inż. Anna Musz-Pomorska	Data:	24.01.2026